

Deed

Version 2.6 released on 7/1/25

PWC 21815

**CITY COUNCIL USE ONLY**

Date Received: _____
 Committee Date: _____
 1st Agenda Date: _____

Tracking #: _____
 Committee: _____
 Hearing Date: _____
 2nd Agenda Date: _____

CITY CLERK USE ONLY

☐ Scanned Date: 03.04.2026
☐ Posted Item #: 2503.00506

*All department items requiring Council approval must be submitted through the Mayor's Office.***Primary Details****Board Approval****Other Board Name****City Council Approval**☒ Yes ☐ No

Department
Public Works

Contact Name
Courtney Jones 02.10.26

Email
courtneyjones@cityoftulsa.org

Phone
918-596-9549

Deed Type
Deed of Dedication

Owner-Grantor
ATMOSS, LLC

Section
8

Township
19

Range
15

Addition
UNPLATTED

Lot

Block

Address
21304 E. 11th ST S.

Parcel
716

Council District
6

Bid/Project
IDP 191978

Related Contract No.

Date Filed Cnty Clerk

County Document Number

Budget**Contract Type**☒ No Payments Involved☐ Revenue Contract☐ Expense Contract**Funding Source(s)****DONATION:**

TOTAL: \$0.00

Approvals

Department: _____

Legal: _____

Board: _____

Mayor: _____

Other: _____

Date: 02.11.26
 Date: 02/24/2026
 Date: MAR 04 2026
 Date: _____

Policy Statement**Background Information**

This Deed of Dedication is being donated by ATMOSS, LLC, a Delaware limited liability company, as a requirement of IDP 191978. This Deed of Dedication is required for infrastructure improvements at Project Anthem.

PDZ: 02/11/26 MSL: 02/10/26 swb

Summary of Requested Actions

Mayoral approval and City Council acceptance.

Other Pertinent Details

Property is located in Wagoner County.

Processing Information for City Clerk's Office**Post Execution Processing**☐ Mail vendor copy (add'l signature copies attached)☒ Must be filed with other governmental entity☐ Add'l governmental entity approval(s) required**Additional Routing and Processing Details**

Original to be picked up by Courtney Jones for further processing. (6-9549)

2026-RF 2-0099

DEED OF DEDICATION

STATE OF OKLAHOMA)
) ss.
COUNTY OF TULSA)

ATMOSS, LLC, a Delaware limited liability company, the undersigned, being the owners of the following described property,

FOR AND IN CONSIDERATION OF the special benefits to the remainder of the property of the above named owners, accruing thereto upon this dedication,

DO HEREBY DEDICATE to the PUBLIC, as public street right-of-way, for the use and enjoyment of the public, the following described real estate and premises, to-wit:

See Exhibit "A"

EXEMPT FROM DOCUMENTARY STAMPS PURSUANT 68 O.S. 3202 (11).

TO HAVE AND TO HOLD the above described premises unto the public forever.

SIGNED AND DELIVERED this 29th day of January, 2026.

ATMOSS, LLC, a Delaware limited liability company

By: _____

Name: Pamela Gregorski

Title: Manager

CITY OF TULSA
OFFICE OF CITY CLERK
175 E. 2ND ST-STE 260
TULSA, OKLAHOMA 74103

STATE OF DELAWARE)
) ss.
COUNTY OF NEW CASTLE)

Before me, the undersigned, a Notary Public, in and for said County and State on this 29th day of January, 2026, personally appeared **Pamela Gregorski**, to me known to be the identical person who subscribed the name of **ATMOSS, LLC, a Delaware limited liability company**, to the foregoing as its **Manager** and acknowledged to me that she executed the same as her free and voluntary act and deed and as the free and voluntary act and deed of **ATMOSS, LLC, a Delaware limited liability company**, for the uses and purposes therein set forth.

Given under my hand and seal of office the day and year last above written.


My commission expires:

05-21-2026



Kelly Anne Piro
Notary Public

APPROVED AS TO FORM:

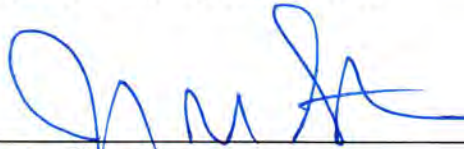

asst. City Attorney

ACCEPTED BY CITY COUNCIL:

Date: _____

APPROVED BY MAYOR:

Date: _____

ATTEST:

City Clerk

APPROVED AS TO SUBSTANCE:



Dep. Director

BY: _____
Name: Karen Gilbert
Title: Chair

CITY OF TULSA, OKLAHOMA,
a municipal corporation

BY: _____
Name: Monroe Nichols IV
Title: Mayor

STATE OF OKLAHOMA)
) ss.
COUNTY OF TULSA)

Before me, a Notary Public in and for said County and State, on the _____ day of _____, 2026, personally appeared Karen Gilbert, to me known to be the identical person who accepted the within and foregoing instrument as Chair of the City Council of the City of Tulsa, Oklahoma, and acknowledged to me that she accepted the within and foregoing instrument as her free and voluntary act and deed and as the free and voluntary act and deed of the City Council of the City of Tulsa, Oklahoma, for the uses and purposes therein set forth.

Notary Public

My commission expires:

STATE OF OKLAHOMA)
) ss.
COUNTY OF TULSA)

Before me, a Notary Public in and for said County and State, on the _____ day of _____, 2026, personally appeared Monroe Nichols IV, to me known to be the identical person who approved the within and foregoing instrument as Mayor of the City of Tulsa, Oklahoma, and acknowledged to me that he approved the within and foregoing instrument as his free and voluntary act and deed and as the free and voluntary act and deed of the City of Tulsa, Oklahoma, for the uses and purposes therein set forth.

Notary Public

My commission expires:

LEGAL DESCRIPTION RIGHT-OF-WAY DEDICATION

For Permanent Right of Way purposes a tract of land lying in the Southwest Quarter (SW/4) of Section Eight (8), Township Nineteen (19) North, Range Fifteen (15) East of the Indian Base and Meridian (I.B. & M.), Wagoner County, Oklahoma, being more particularly described by Darrel Ray Mason OKLS1690 on May 22, 2025 as follows:

COMMENCING at the Southeast Corner of the Southwest Quarter, Section 8, Township 19 North, Range 15 East of the I.B.M, Thence along the South line of said Southwest Quarter, as the basis of bearings, S 88° 59' 21" W a distance of 210.46 feet to the POINT OF BEGINNING;
Thence continuing along said South section line, S 88° 59' 21" W, a distance of 2,427.99 feet to the Southwest Corner of the Southwest Quarter; Thence along the West Section line of said Section 8, N 01° 35' 54" W, a distance of 50.00 feet; Thence departing said West section line 50.00 feet North of and parallel to the South line of said Southwest Quarter, N 88° 59' 21" E, a distance of 2,428.56 feet; Thence S 00° 56' 43" E, a distance of 50.00 feet back to the POINT OF BEGINNING.

This description contains 121,410 sq. ft. or 2.787 acres, more or less.

Basis of Bearings:

S 88° 59' 21" W along South line said SW/4.8-T19N-R15E
Grid, based on NAD 83 Oklahoma State Plane Coordinate System North Zone

Date of last visit: 8-21-2024

I, Darrel Ray Mason, a Licensed Professional Land Surveyor in the State of Oklahoma, certify that the attached description is a true representation of the property described and meets the minimum technical standards for land surveying of the State of Oklahoma.



[Signature] 5/23/25
Darrel Ray Mason Date



OK PLS NO. 1690 - Expires August 31, 2026
OK CA NO. 2483 - Expires June 30, 2025

PROJECT NO: 022-02495	PROPOSED DESCRIPTION R.O.W. PARCEL		11600 Broadway Extension Suite 300 Oklahoma City, OK 73114 olsson.com TEL 405.242.6600 Olsson - Survey Oklahoma COA #2483	EXHIBIT A
DRAWN BY: TLM				
DATE: 03.21.2025				

EXHIBIT "A"

**PLAT OF SURVEY
RIGHT-OF-WAY DEDICATION**

EB JMS

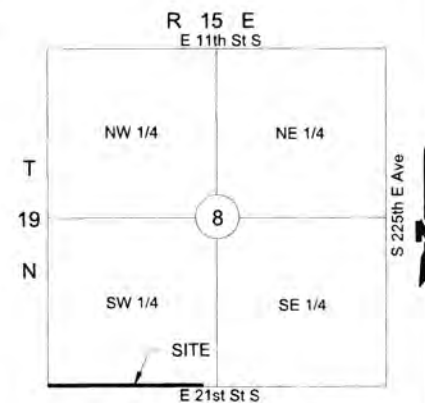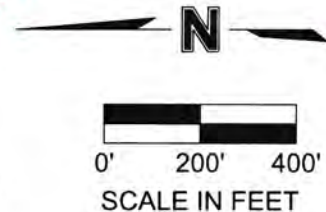

LOCATION MAP

NOT TO SCALE

BASIS OF BEARING

Oklahoma State Plane NAD83
Oklahoma North Zone
S88°59'21"W
Along the South Line of said SW/4
8-T19N-R15E


I, DARREL RAY MASON, OF OLSSON, CERTIFY THAT THE ATTACHED PLAT OF SURVEY IS A TRUE REPRESENTATION OF THE RIGHT OF WAY AS DESCRIBED, AND MEETS THE MINIMUM TECHNICAL STANDARDS FOR LAND SURVEYING OF THE STATE OF OKLAHOMA.

DATE OF LAST VISIT: 8-21-2024



LEGEND

- SECTION CORNER
- SET 1/2" REBAR W/ CAP "OLSSON CA 2483"
- SECTION LINE
- STATUTORY R.O.W.
- NEW R.O.W.
- TEMPORARY CONSTRUCTION

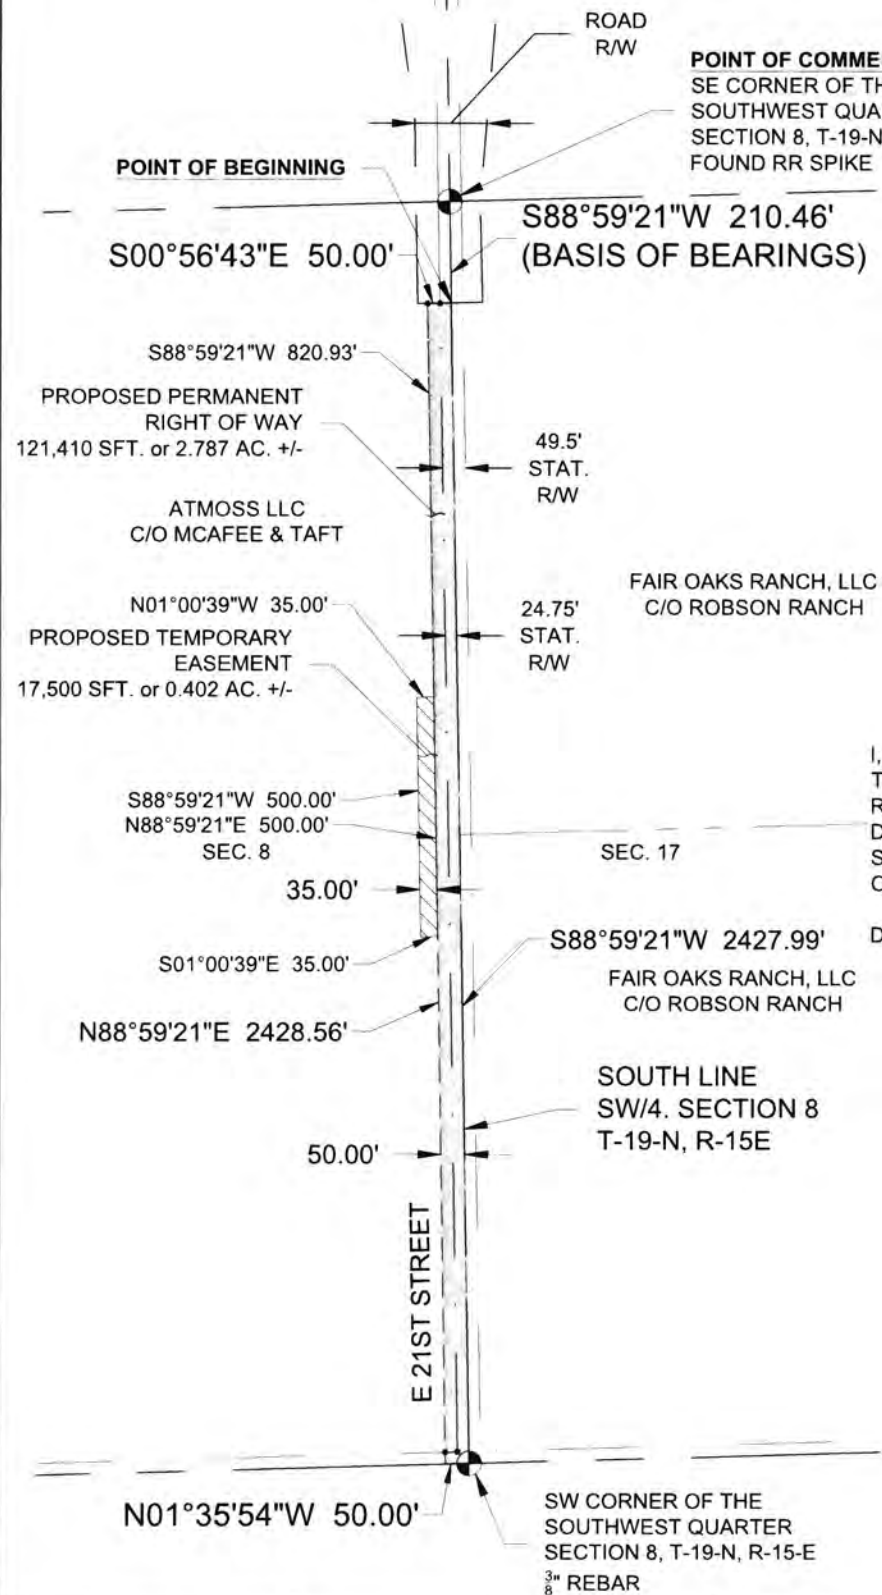

PROJECT NO: 022-02495
DRAWN BY: TLM
DATE: 03.21.2025

**EXHIBIT
R.O.W. PARCEL**



11600 Broadway Extension
Suite 300
Oklahoma City, OK 73114
olsson.com
TEL 405.242.6600
Olsson - Survey
Oklahoma COA #2483

**EXHIBIT
A**

EXHIBIT "A"

F:\2022\02001-02500\022-02495\40-Design\Survey\SRV\Xref\Robson\Easements\Proposed ROW Acquisition\Proposed ROW Acquisition\IV_PESMT_2202495_1.dwg
DATE: May 20, 2025 5:36pm USER: tmason